




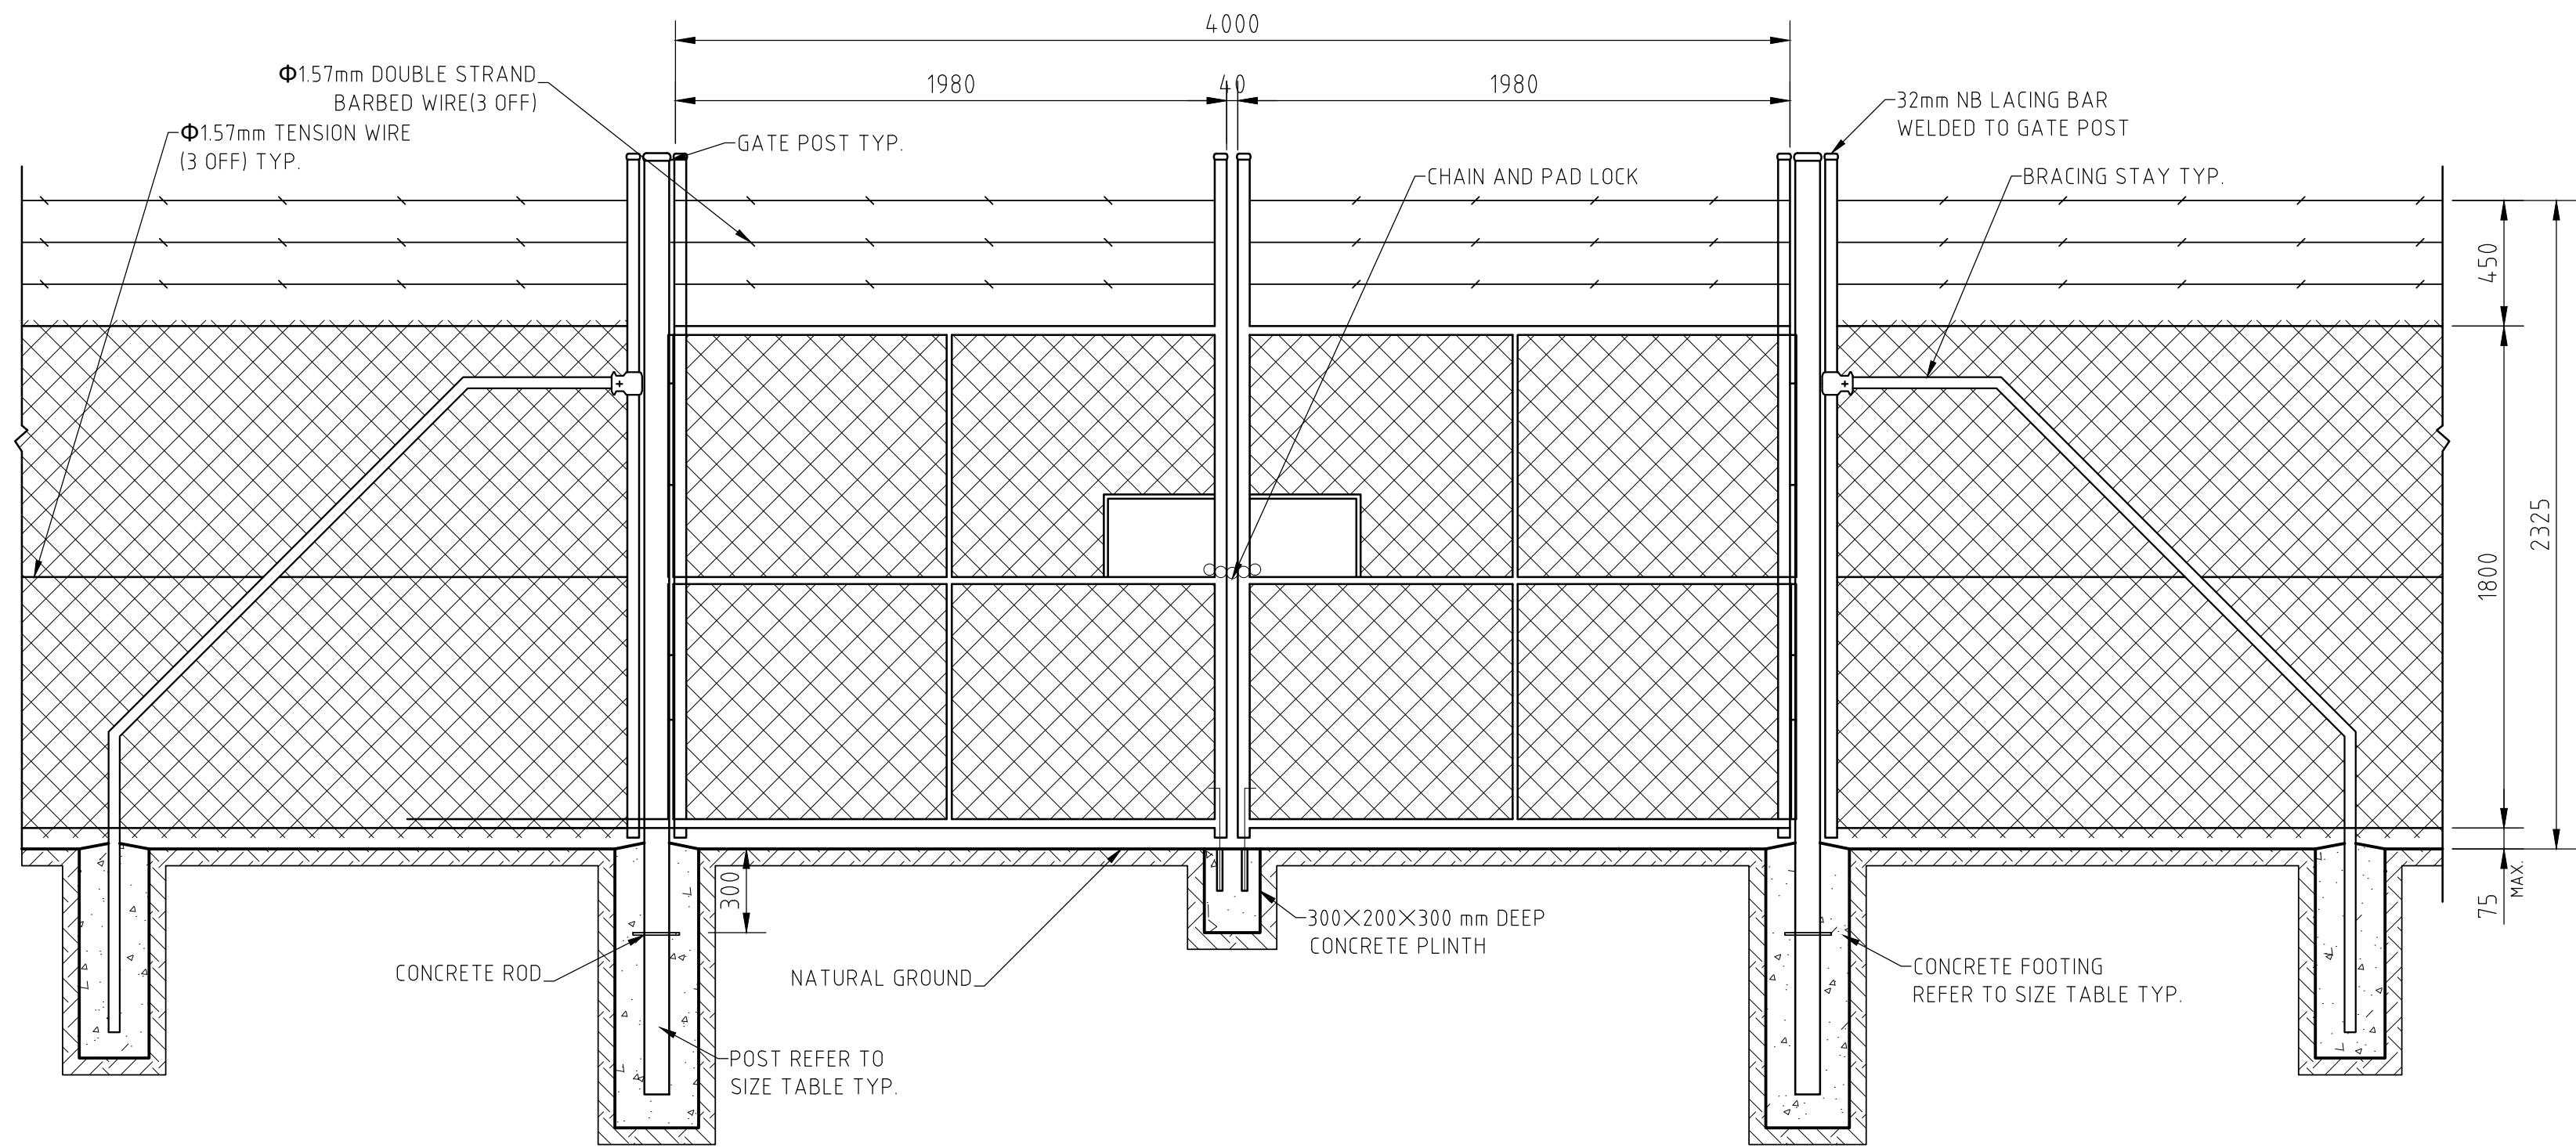


CHAIN LINK FABRIC FENCE AND OPENING DOUBLE GATE -4000 GATE
SCALE 1:20

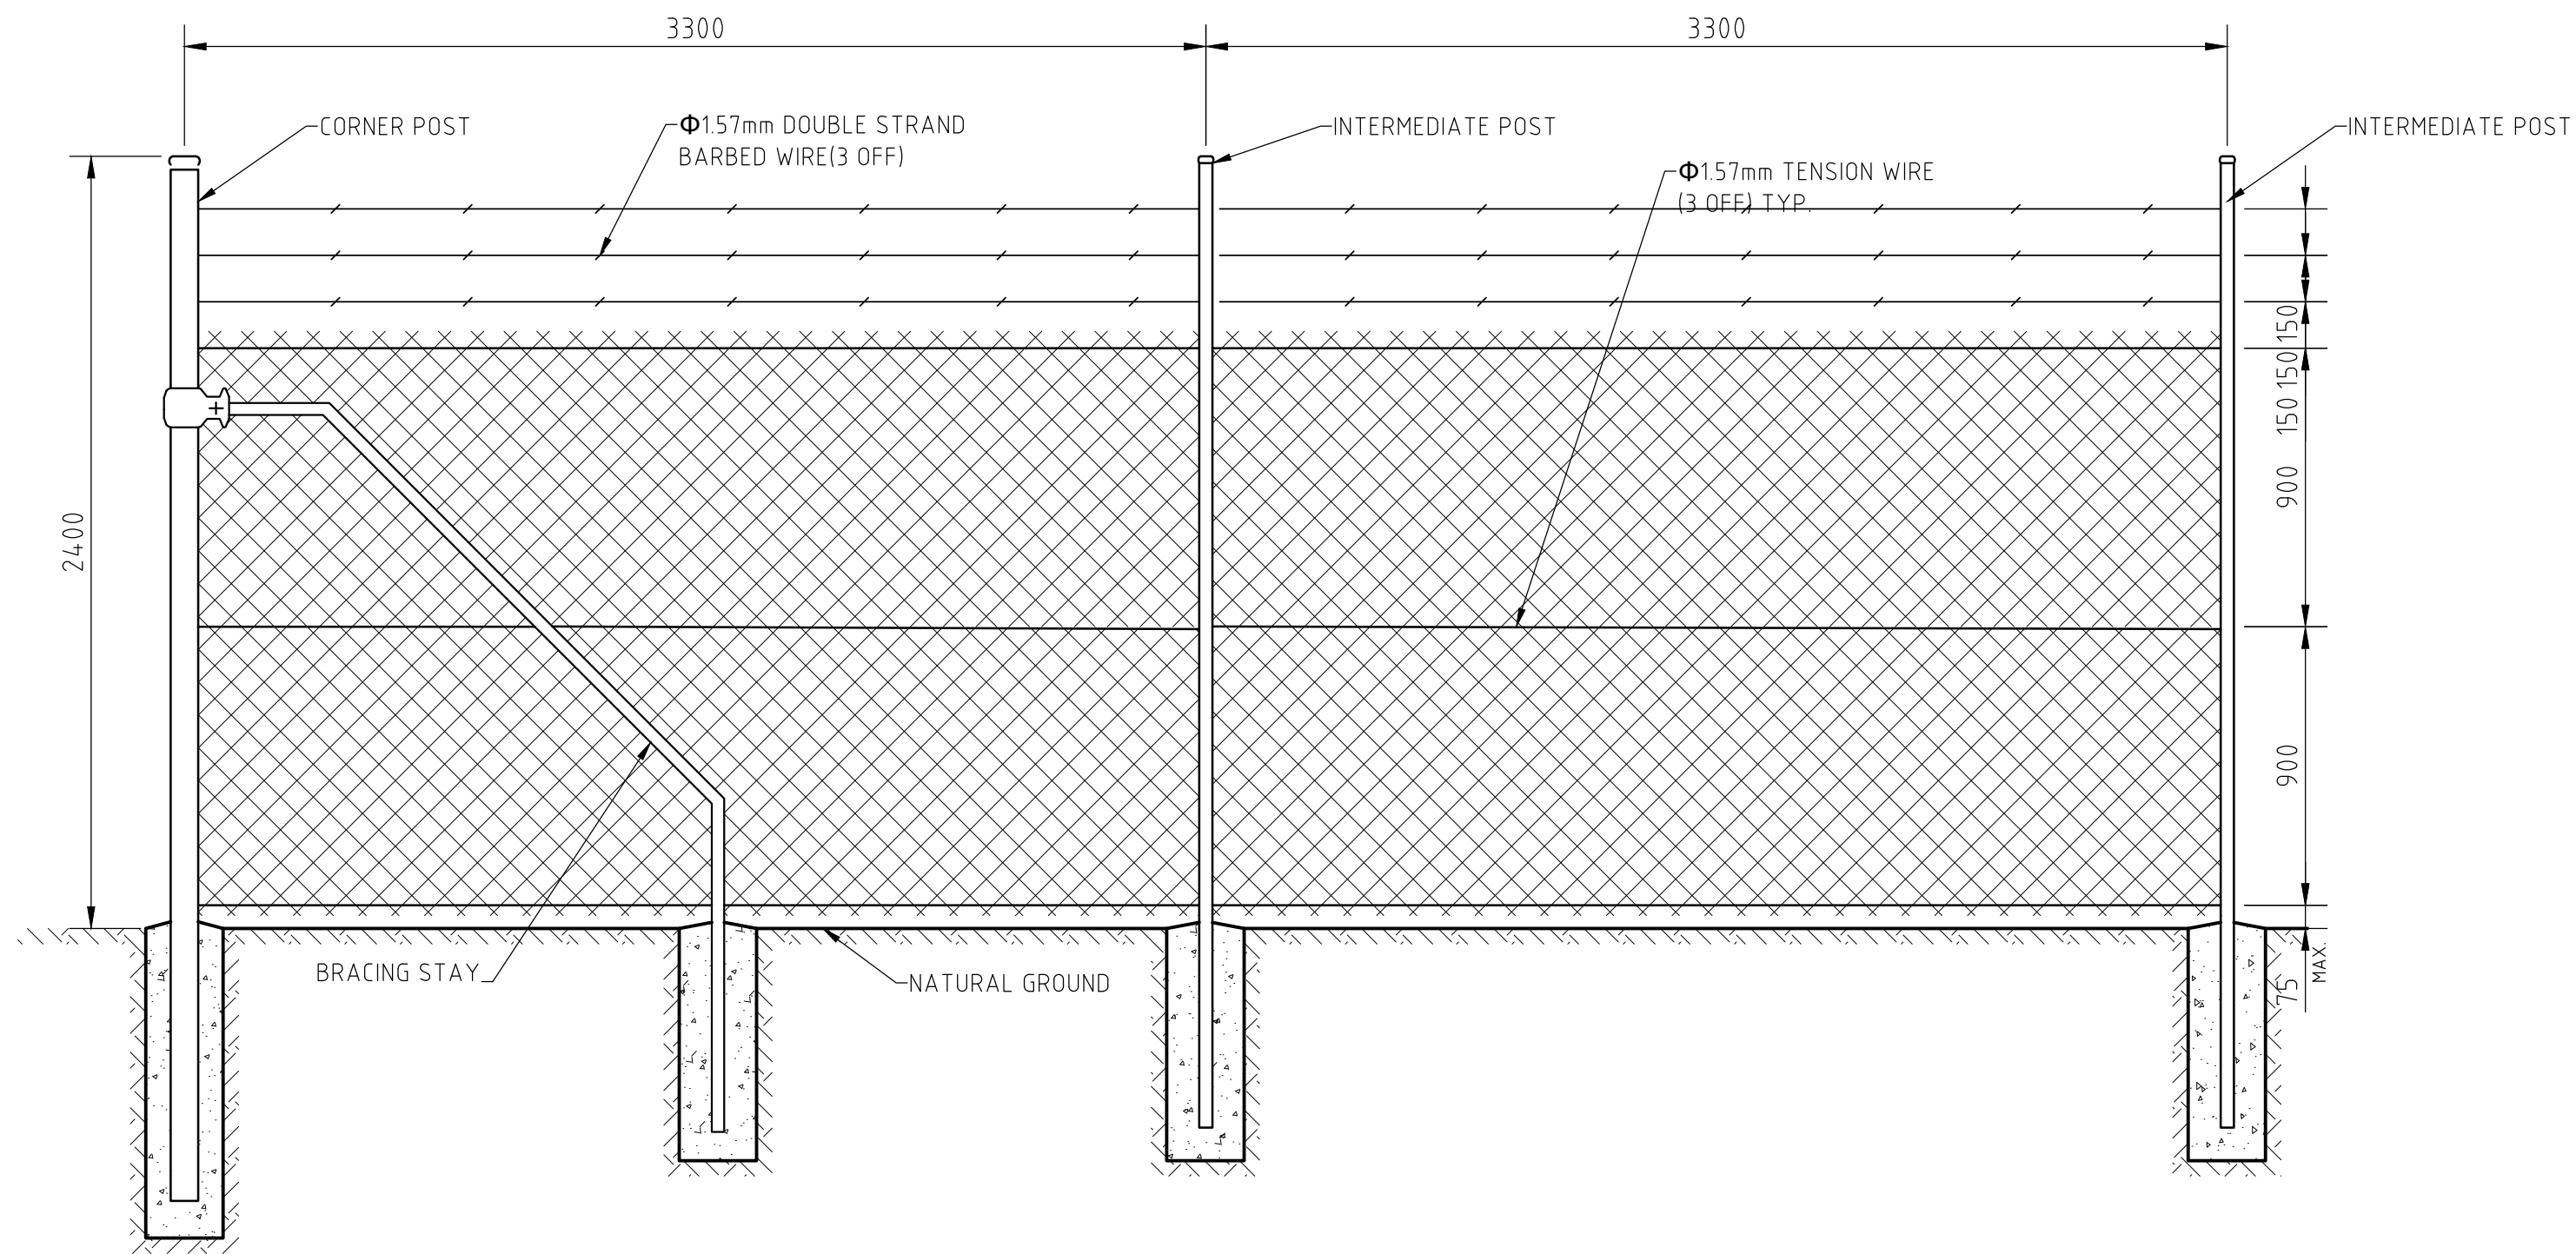

TYPICAL CHAIN MESH FENCE PANEL-3300 DISTANCE
SCALE 1:20

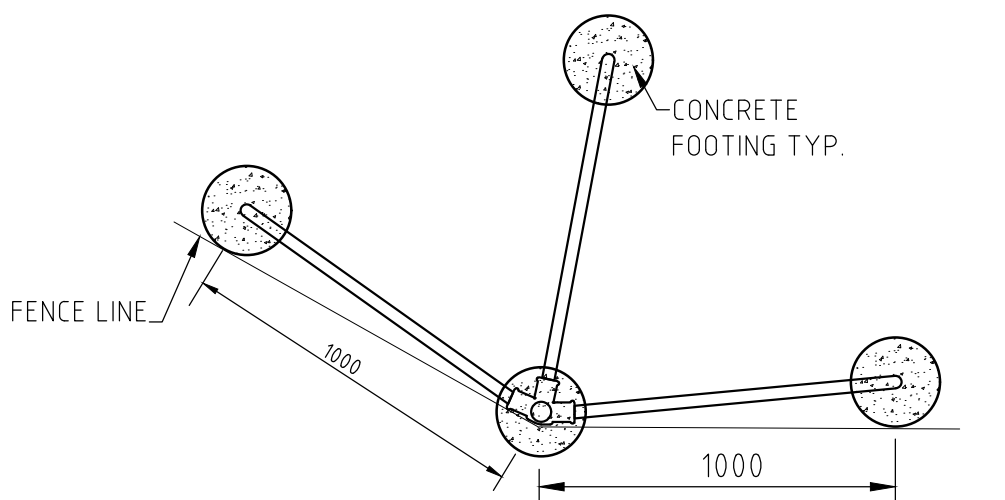

CORNER POST FOOTING PLAN(>90)
SCALE 1:20

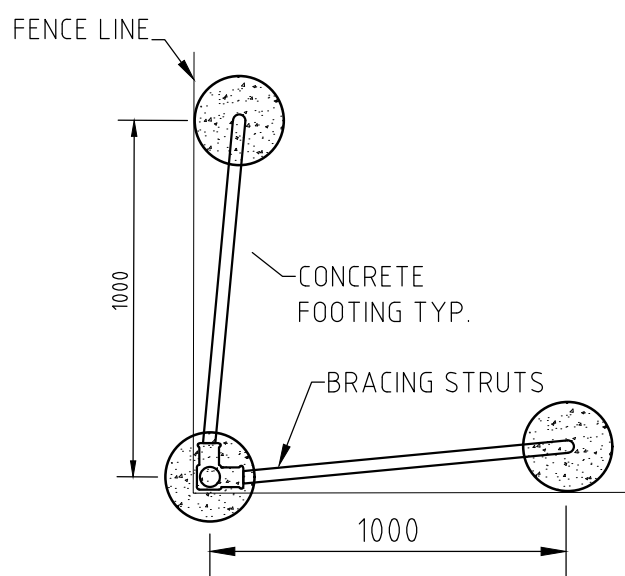

CORNER POST FOOTING PLAN(<90)
SCALE 1:20

NOTES

- CHAIN LINK FABRIC TO BE CLASS 2 TYPE 1-R-L/B-T RAILED LESS 3 BARBED TOP SECURITY FENCING AS PER AS1725.1.
- CHAIN LINK FABRIC TO BE ZINC/ALUM-ALLOY 2.50mm (LIGHT DUTY) WIRE WITH 50MM NOMINAL PITCH MESH (OR SIMILAR APPROVED)
- SUPPORT CABLE TO BE 4mm SINGLE STRAND WITH ZINC/ALUM-ALLOY COATING (OR SIMILAR APPROVED)
- LACING WIRE TO BE 2mm WITH ZINC/ALUM-ALLOY COATING (OR SIMILAR APPROVED)
- CONCRETE FOOTING SHALL BE IN ACCORDANCE WITH AS3600, AND NOT LESS THAN THE MINIMUM SIZE SPECIFIED IN THIS DRAWING.
- CONCRETE SHALL HAVE A CHARACTERISTIC COMPRESSIVE STRENGTH AT 28 DAYS OF 25MPA
- GATES SHALL BE DESIGNED FOR BOTH INWARDS AND OUTWARDS OPENING
- GATE DETAILS PROVIDED ON THIS DRAWING ARE TO BE USED AS ALTERNATIVE TO THE DRAWINGS PLC FENCING PROVIDE.
- THIS DRAWING IS TO BE READ IN CONJUNCTION WITH AS1725.1 AND PLC FENCING DRAWING AND DESIGN
- ALL DIMENSIONS MENTIONED IN THIS DRAWING ARE IN mm, OR OTHERWISE SPECIFIED.

POST				FOOTING SIZE	
TYPE	DN	O.D	WALL	DIA	DEPTH
CORNER	DN 50	60.3	3.6	250	750
INTERMEDIATE	DN 40	48.3	2.9	250	600
BRACING STAY	DN 32	42.4	2.6	250	600


DOUBLE ACCESS GATES					
WIDTH OF GATE OPENING	GATE POST			FOOTING	
	DN	O.D	WALL	DIA	DEPTH
4000	DN 80	88.9	4	300	900

FOR CONSTRUCTION
FOR REVIEW


	A	20/11/25	ACE	MG	AW	GG23	ISSUED FOR REVIEW			
	No	DATE	DES	DRN	APP	PROJECT	DESCRIPTION	NUMBER	TITLE	
CLIENT	REVISION								REFERENCE DRAWINGS	




S445 1074 COPPER COAST HIGHWAY SOUTH HUMMOCKS SA DATA CENTRE PROJECT FENCE & GATE LAYOUT PLAN					
DESIGNED BY ACE, ALLIED CONSULTING ENGINEERS			SCALE: NTS		
PROJ No GG23	DRG No GG23-C-PLN-003		REV A		

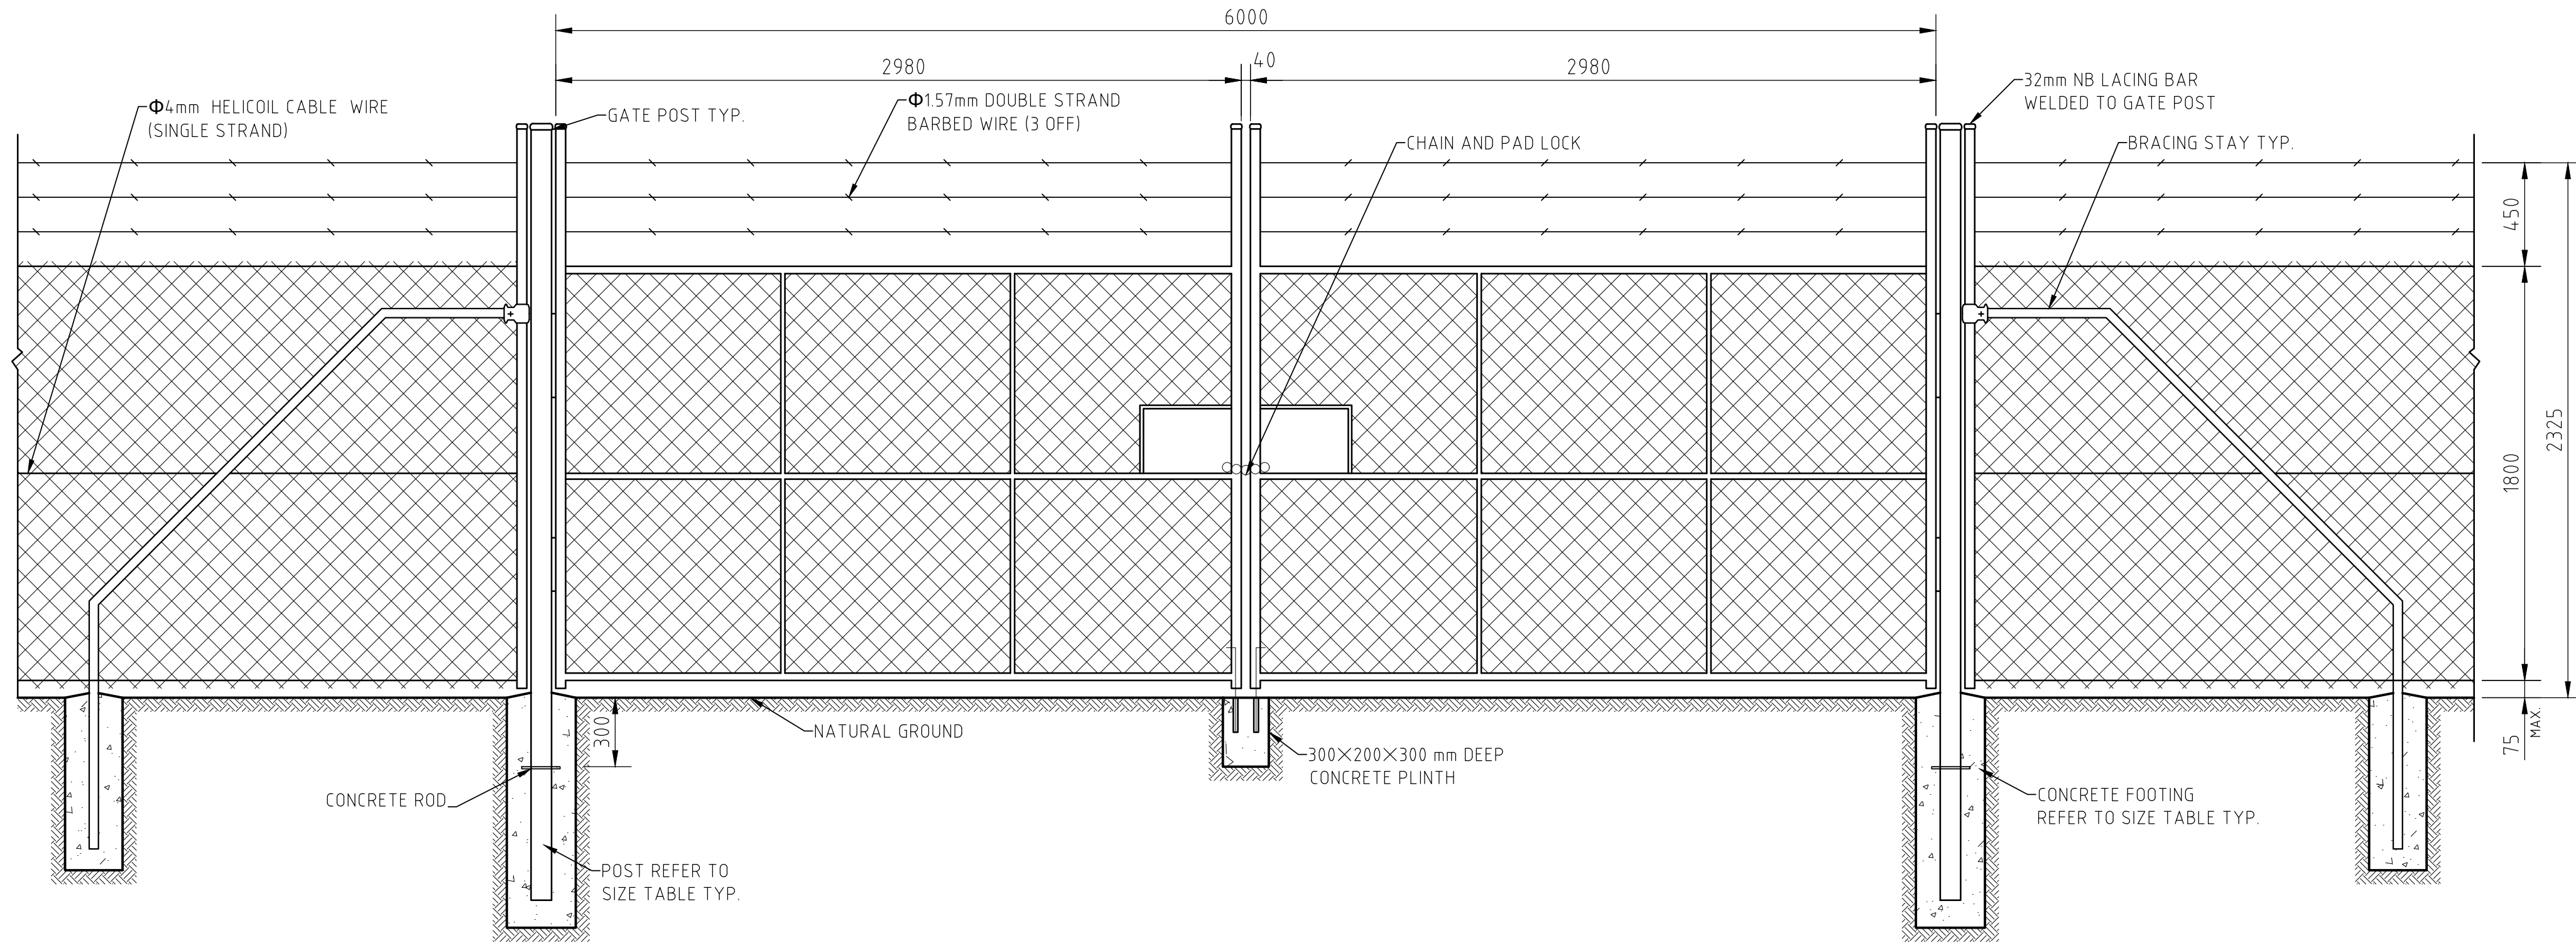


CHAIN LINK FABRIC FENCE AND OPENING DOUBLE GATE - 6000 GATE
SCALE 1:20

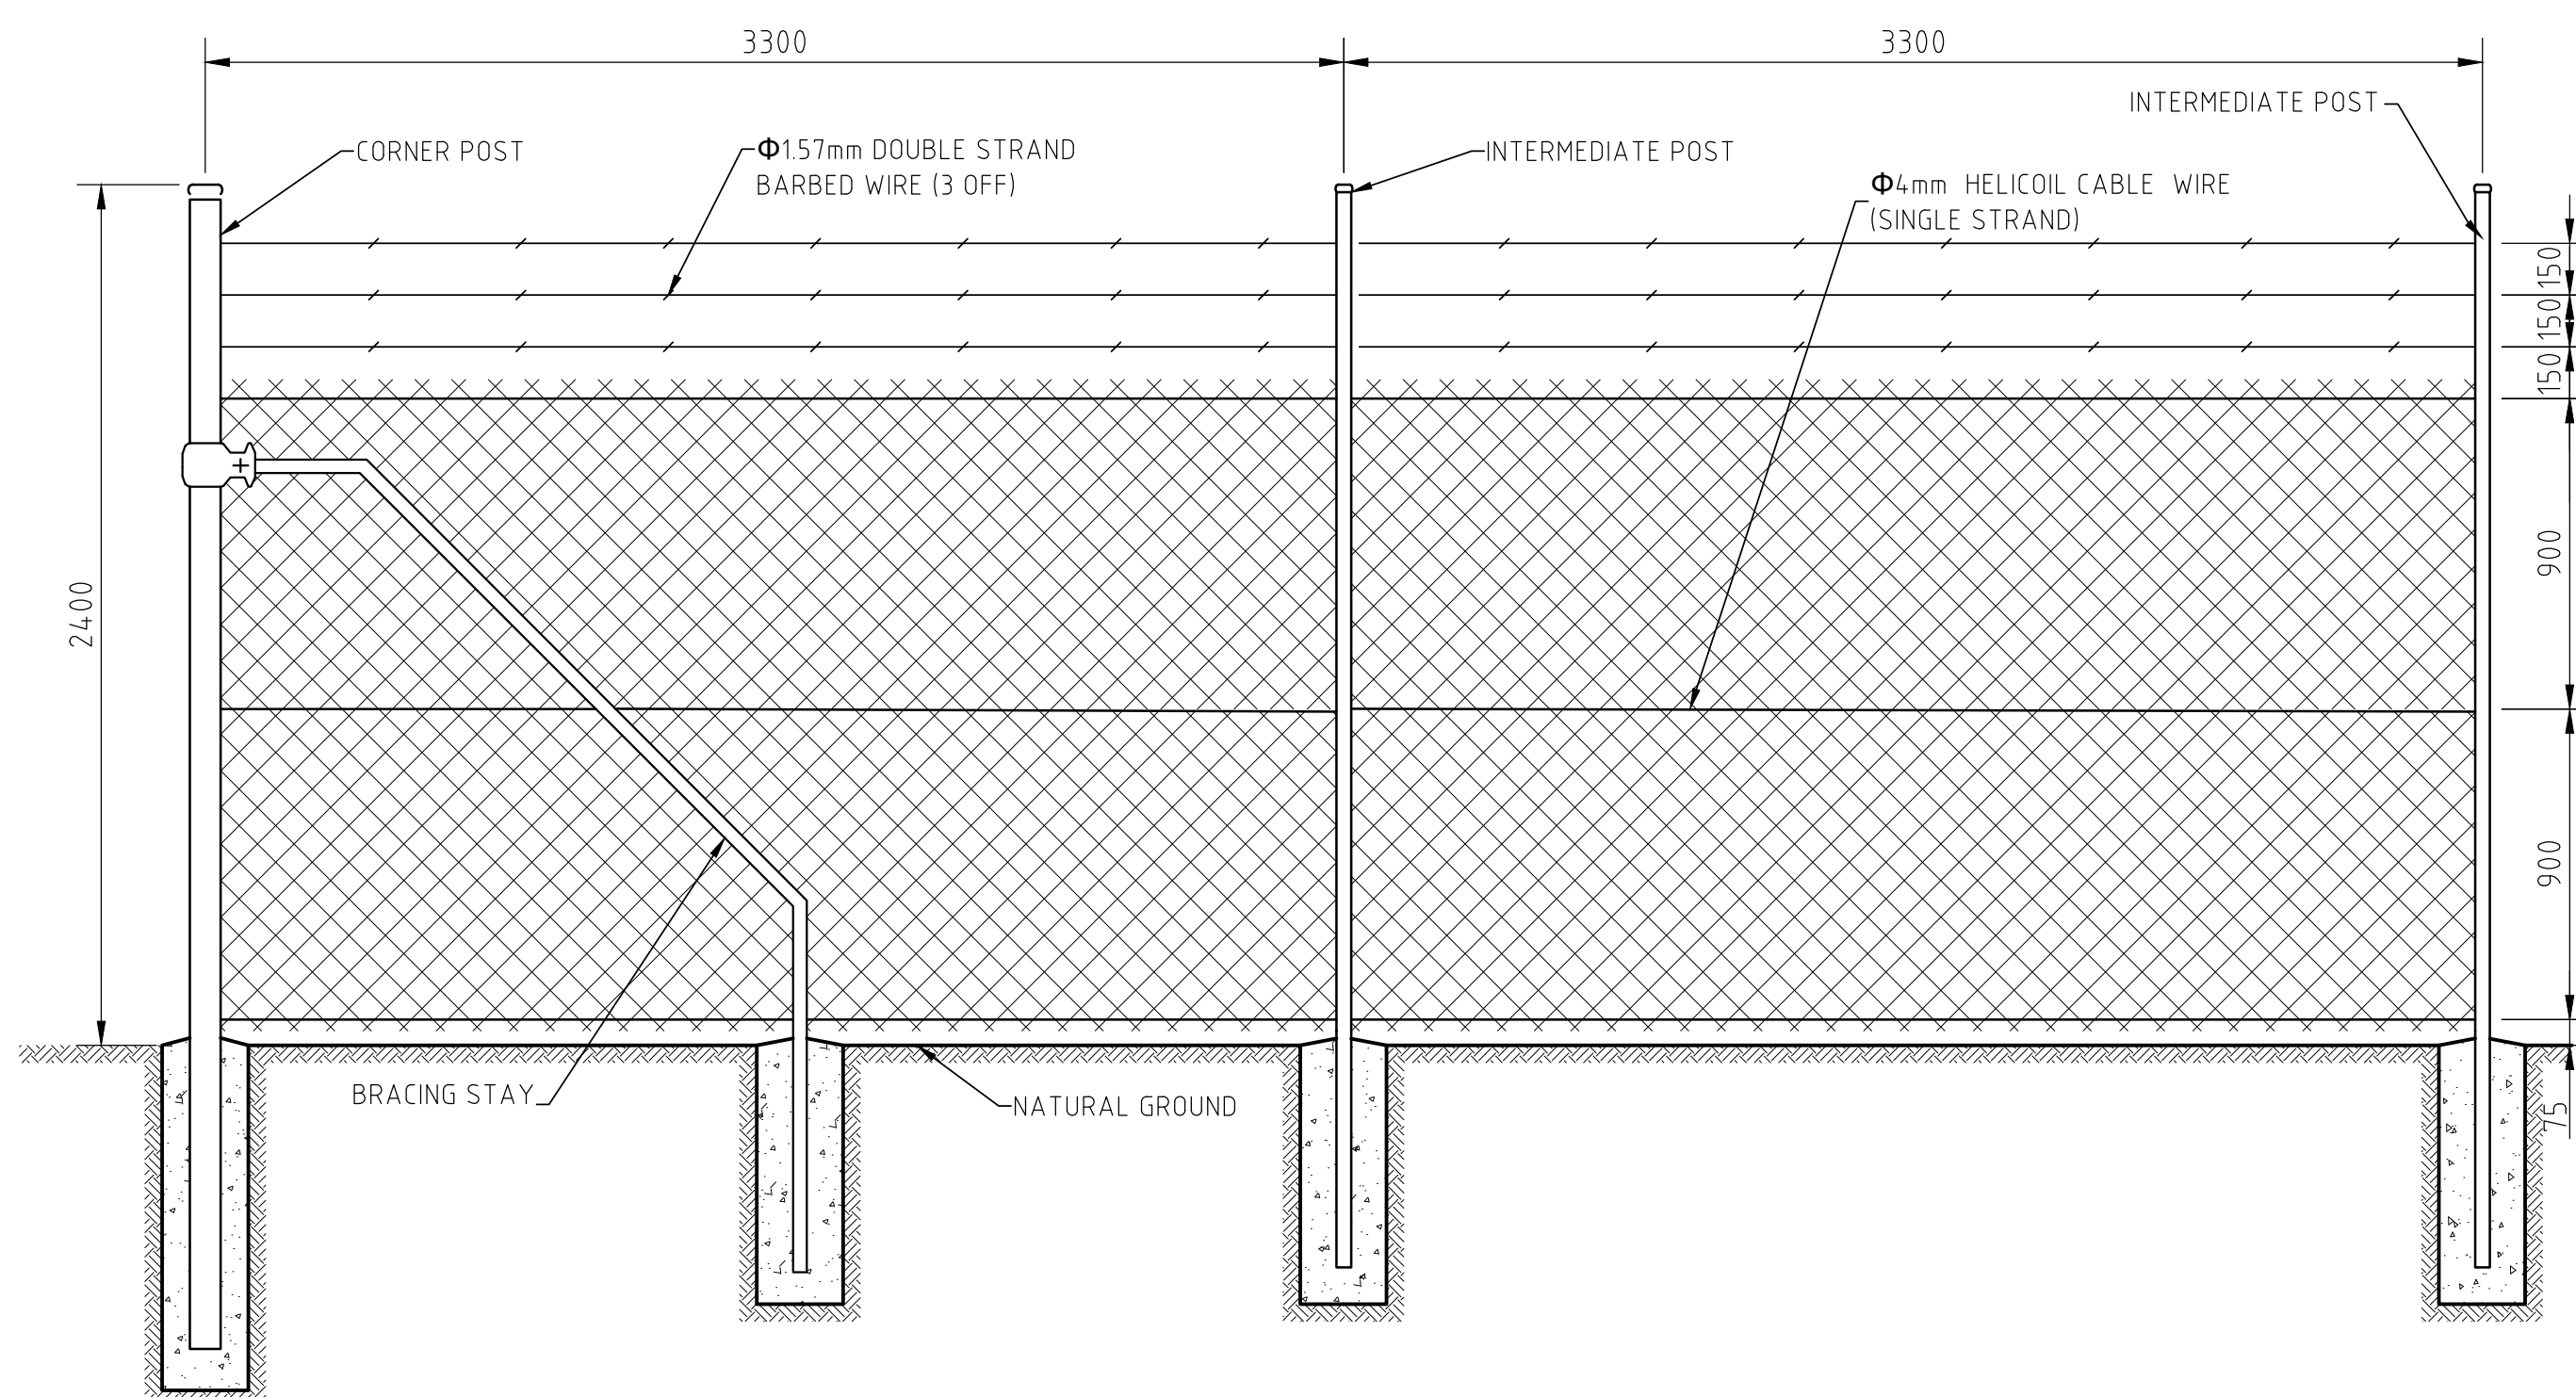

TYPICAL CHAIN MESH FENCE PANEL - 3300 DISTANCE
SCALE 1:20

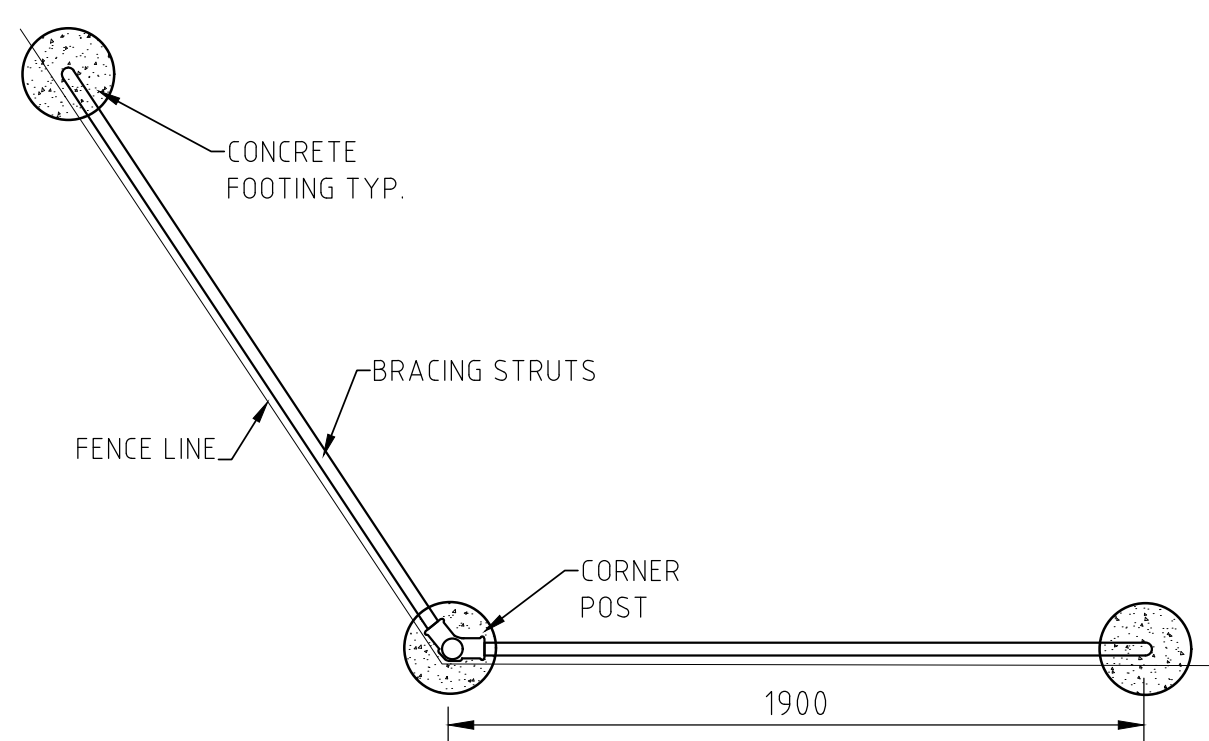

CORNER POST FOOTING PLAN (>90)
SCALE 1:20

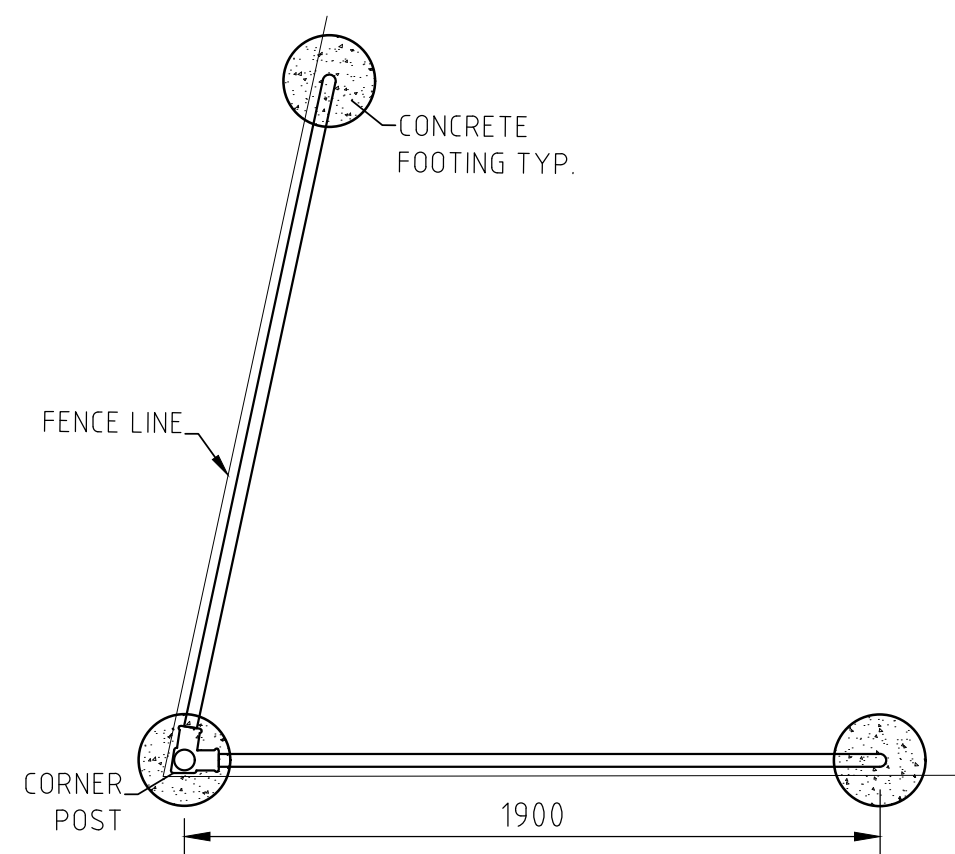

CORNER POST FOOTING PLAN (<90)
SCALE 1:20

NOTES

1. CHAIN LINK FABRIC TO BE CLASS 2 TYPE 1-R-L/B-T RAILED LESS 3 BARBED TOP SECURITY FENCING AS PER AS1725.1.
2. CHAIN LINK FABRIC TO BE ZINC/ALUM-ALLOY 2.50mm (LIGHT DUTY) WIRE WITH 50MM NOMINAL PITCH MESH (OR SIMILAR APPROVED)
3. SUPPORT CABLE TO BE 4mm SINGLE STRAND WITH ZINC/ALUM-ALLOY COATING (OR SIMILAR APPROVED)
4. LACING WIRE TO BE 2mm WITH ZINC/ALUM-ALLOY COATING (OR SIMILAR APPROVED)
5. CONCRETE FOOTING SHALL BE IN ACCORDANCE WITH AS3600, AND NOT LESS THAN THE MINIMUM SIZE SPECIFIED IN THIS DRAWING.
6. CONCRETE SHALL HAVE A CHARACTERISTIC COMPRESSIVE STRENGTH AT 28 DAYS OF 25MPA
7. GATES SHALL BE DESIGNED FOR BOTH INWARDS AND OUTWARDS OPENING
8. GATE DETAILS PROVIDED ON THIS DRAWING ARE TO BE USED AS ALTERNATIVE TO THE DRAWINGS PLC FENCING PROVIDE.
9. THIS DRAWING IS TO BE READ IN CONJUNCTION WITH AS1725.1 AND PLC FENCING DRAWING AND DESIGN
10. ALL DIMENSIONS MENTIONED IN THIS DRAWING ARE IN mm, OR OTHERWISE SPECIFIED.

POST				FOOTING SIZE	
TYPE	DN	O.D	WALL	DIA	DEPTH
CORNER	DN 50	60.3	3.6	250	750
INTERMEDIATE	DN 40	48.3	2.9	250	600
BRACING STAY	DN 32	42.4	2.6	250	600

DOUBLE ACCESS GATES					
WIDTH OF GATE OPENING	GATE POST			FOOTING	
	DN	O.D	WALL	DIA	DEPTH
6000	DN 80	88.9	4	300	1000

A	16/12/25	DS	AW	ACE	AW	GG31	ISSUED FOR REVIEW
No	DATE	DRN	CHK	ENG	APP	PROJECT	DESCRIPTION
CLIENT				REVISION			NUMBER
							TITLE
							REFERENCE DRAWINGS

11544 AUGUSTA HIGHWAY, WARNERTOWN SA 5540
4.98MVA BESS EXPORT SYSTEM
FENCE & GATE LAYOUT PLAN

DESIGNED BY ALLIED CONSULTING ENGINEERS
PROJ No GG31
DRG No GG31-C-PLN-003

SCALE: NST
PAGE: 1
REV A

FOR REVIEW