



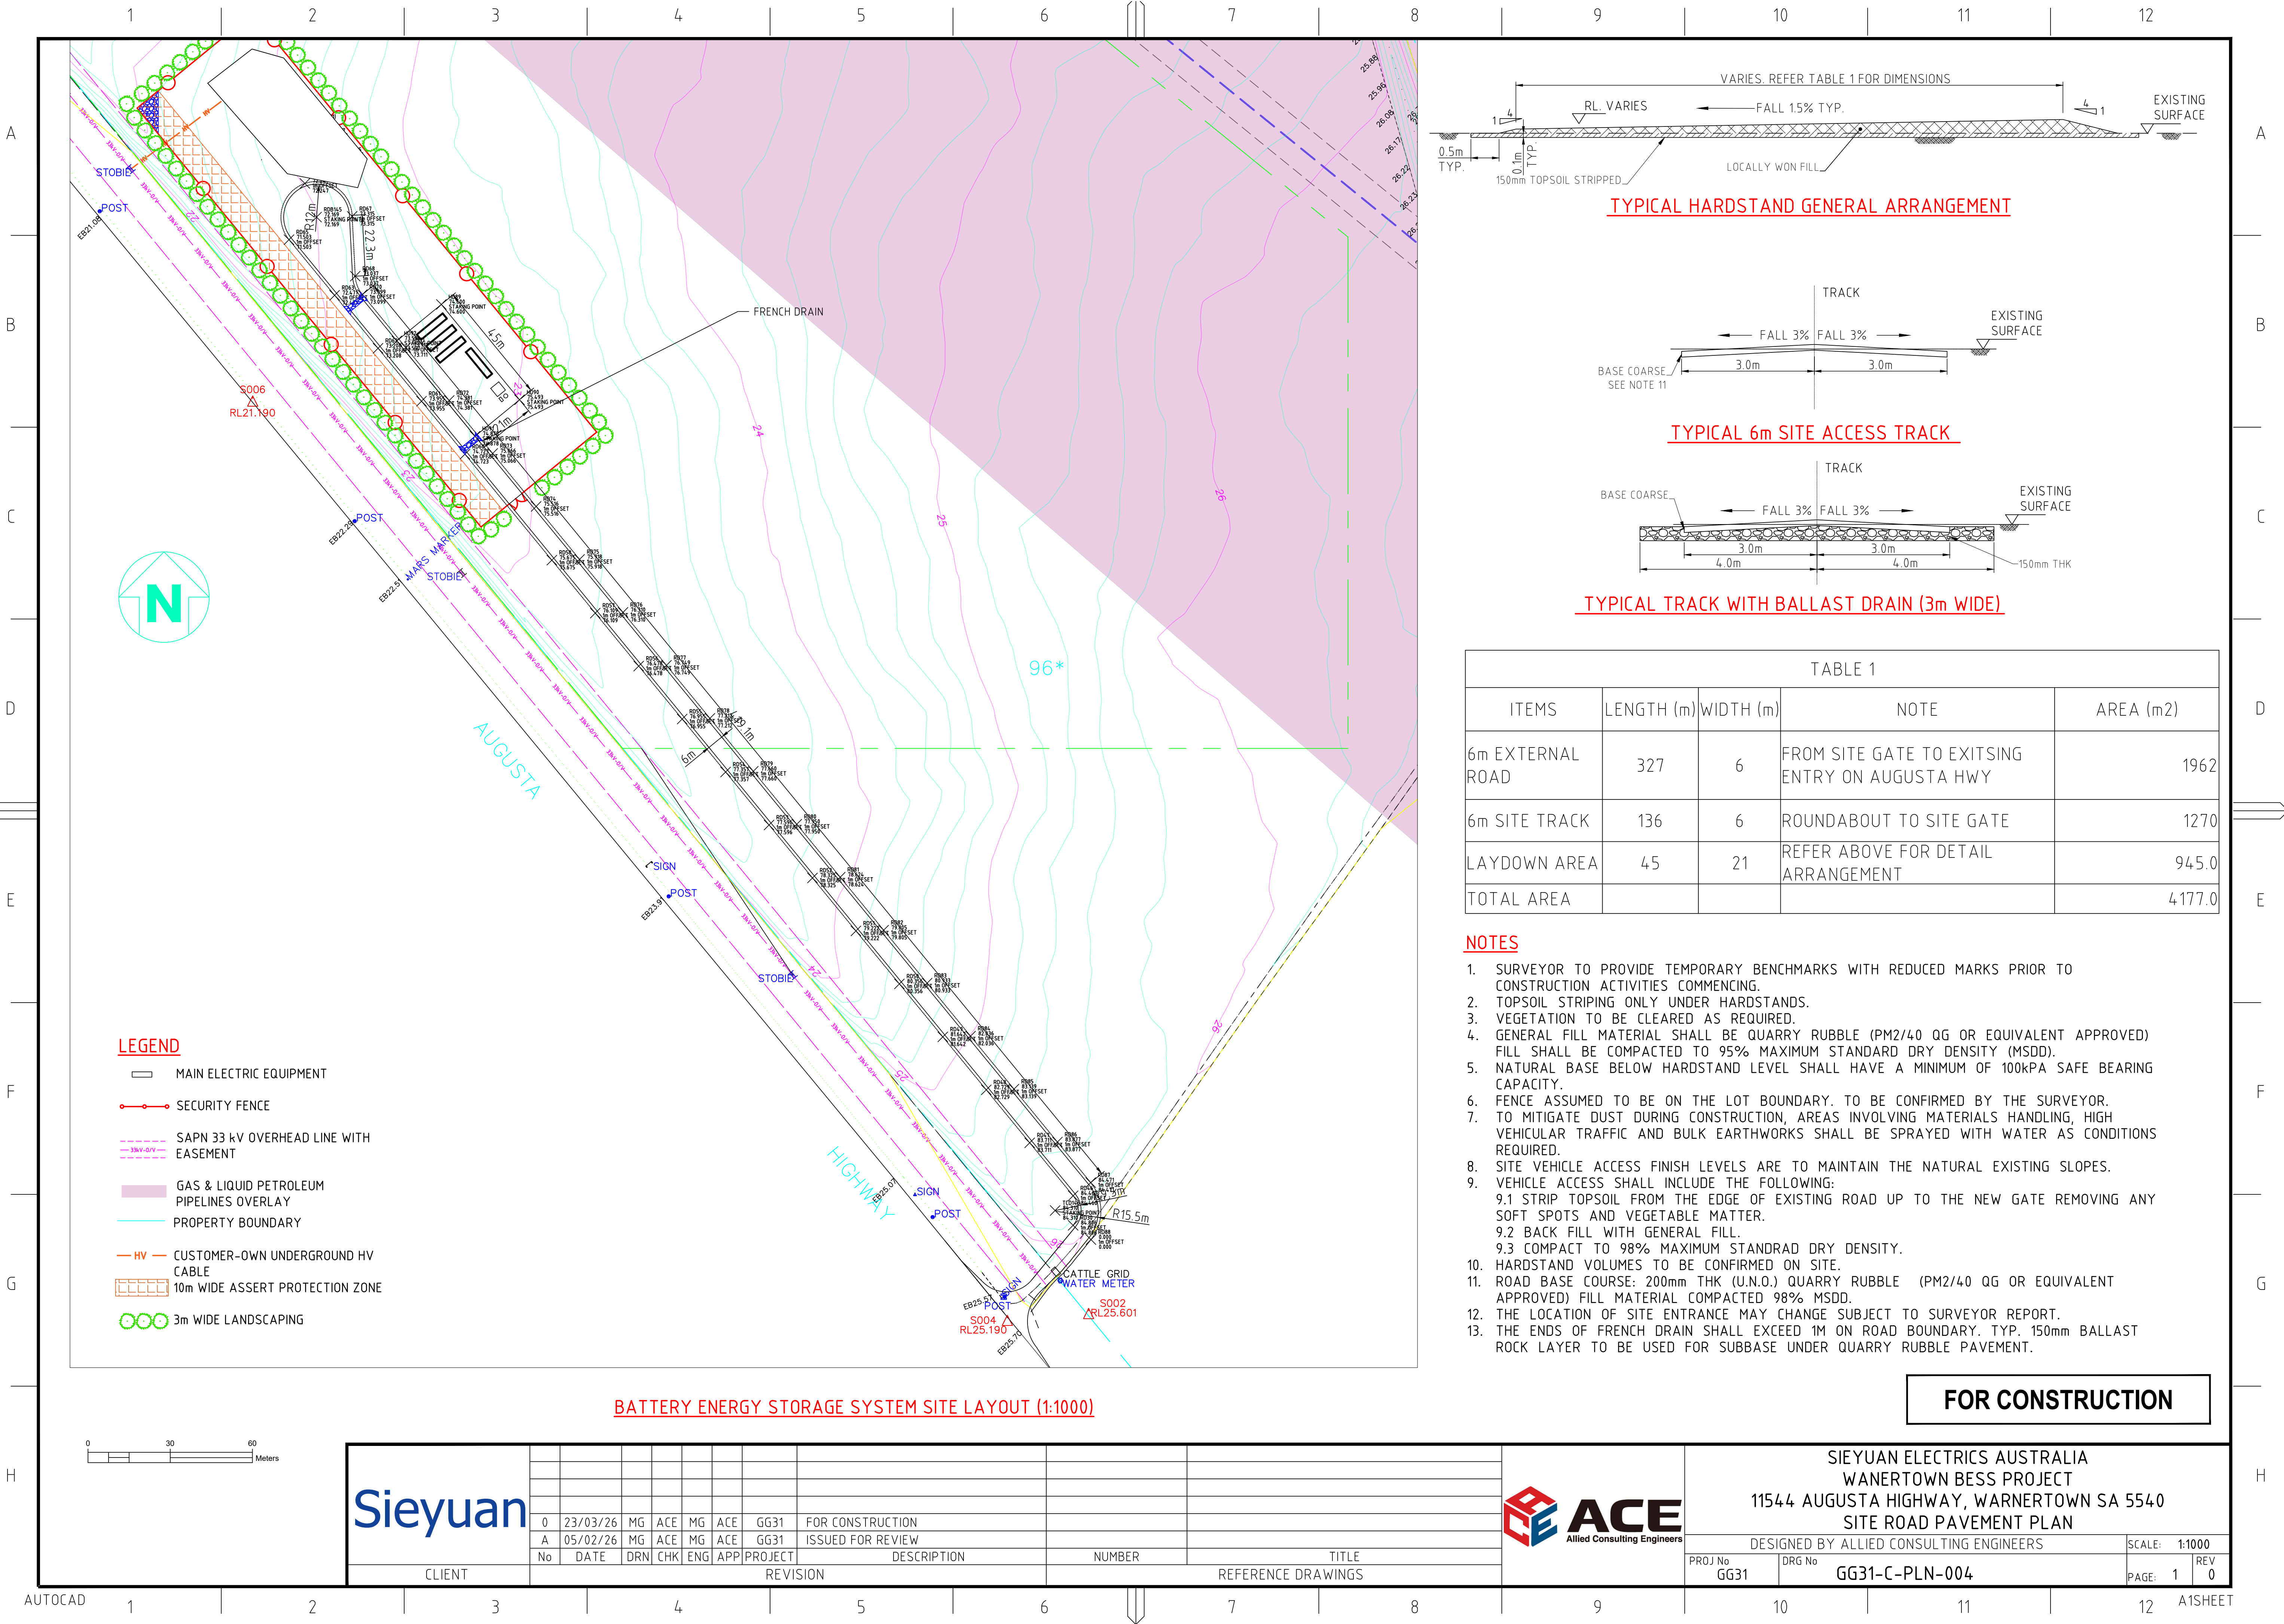

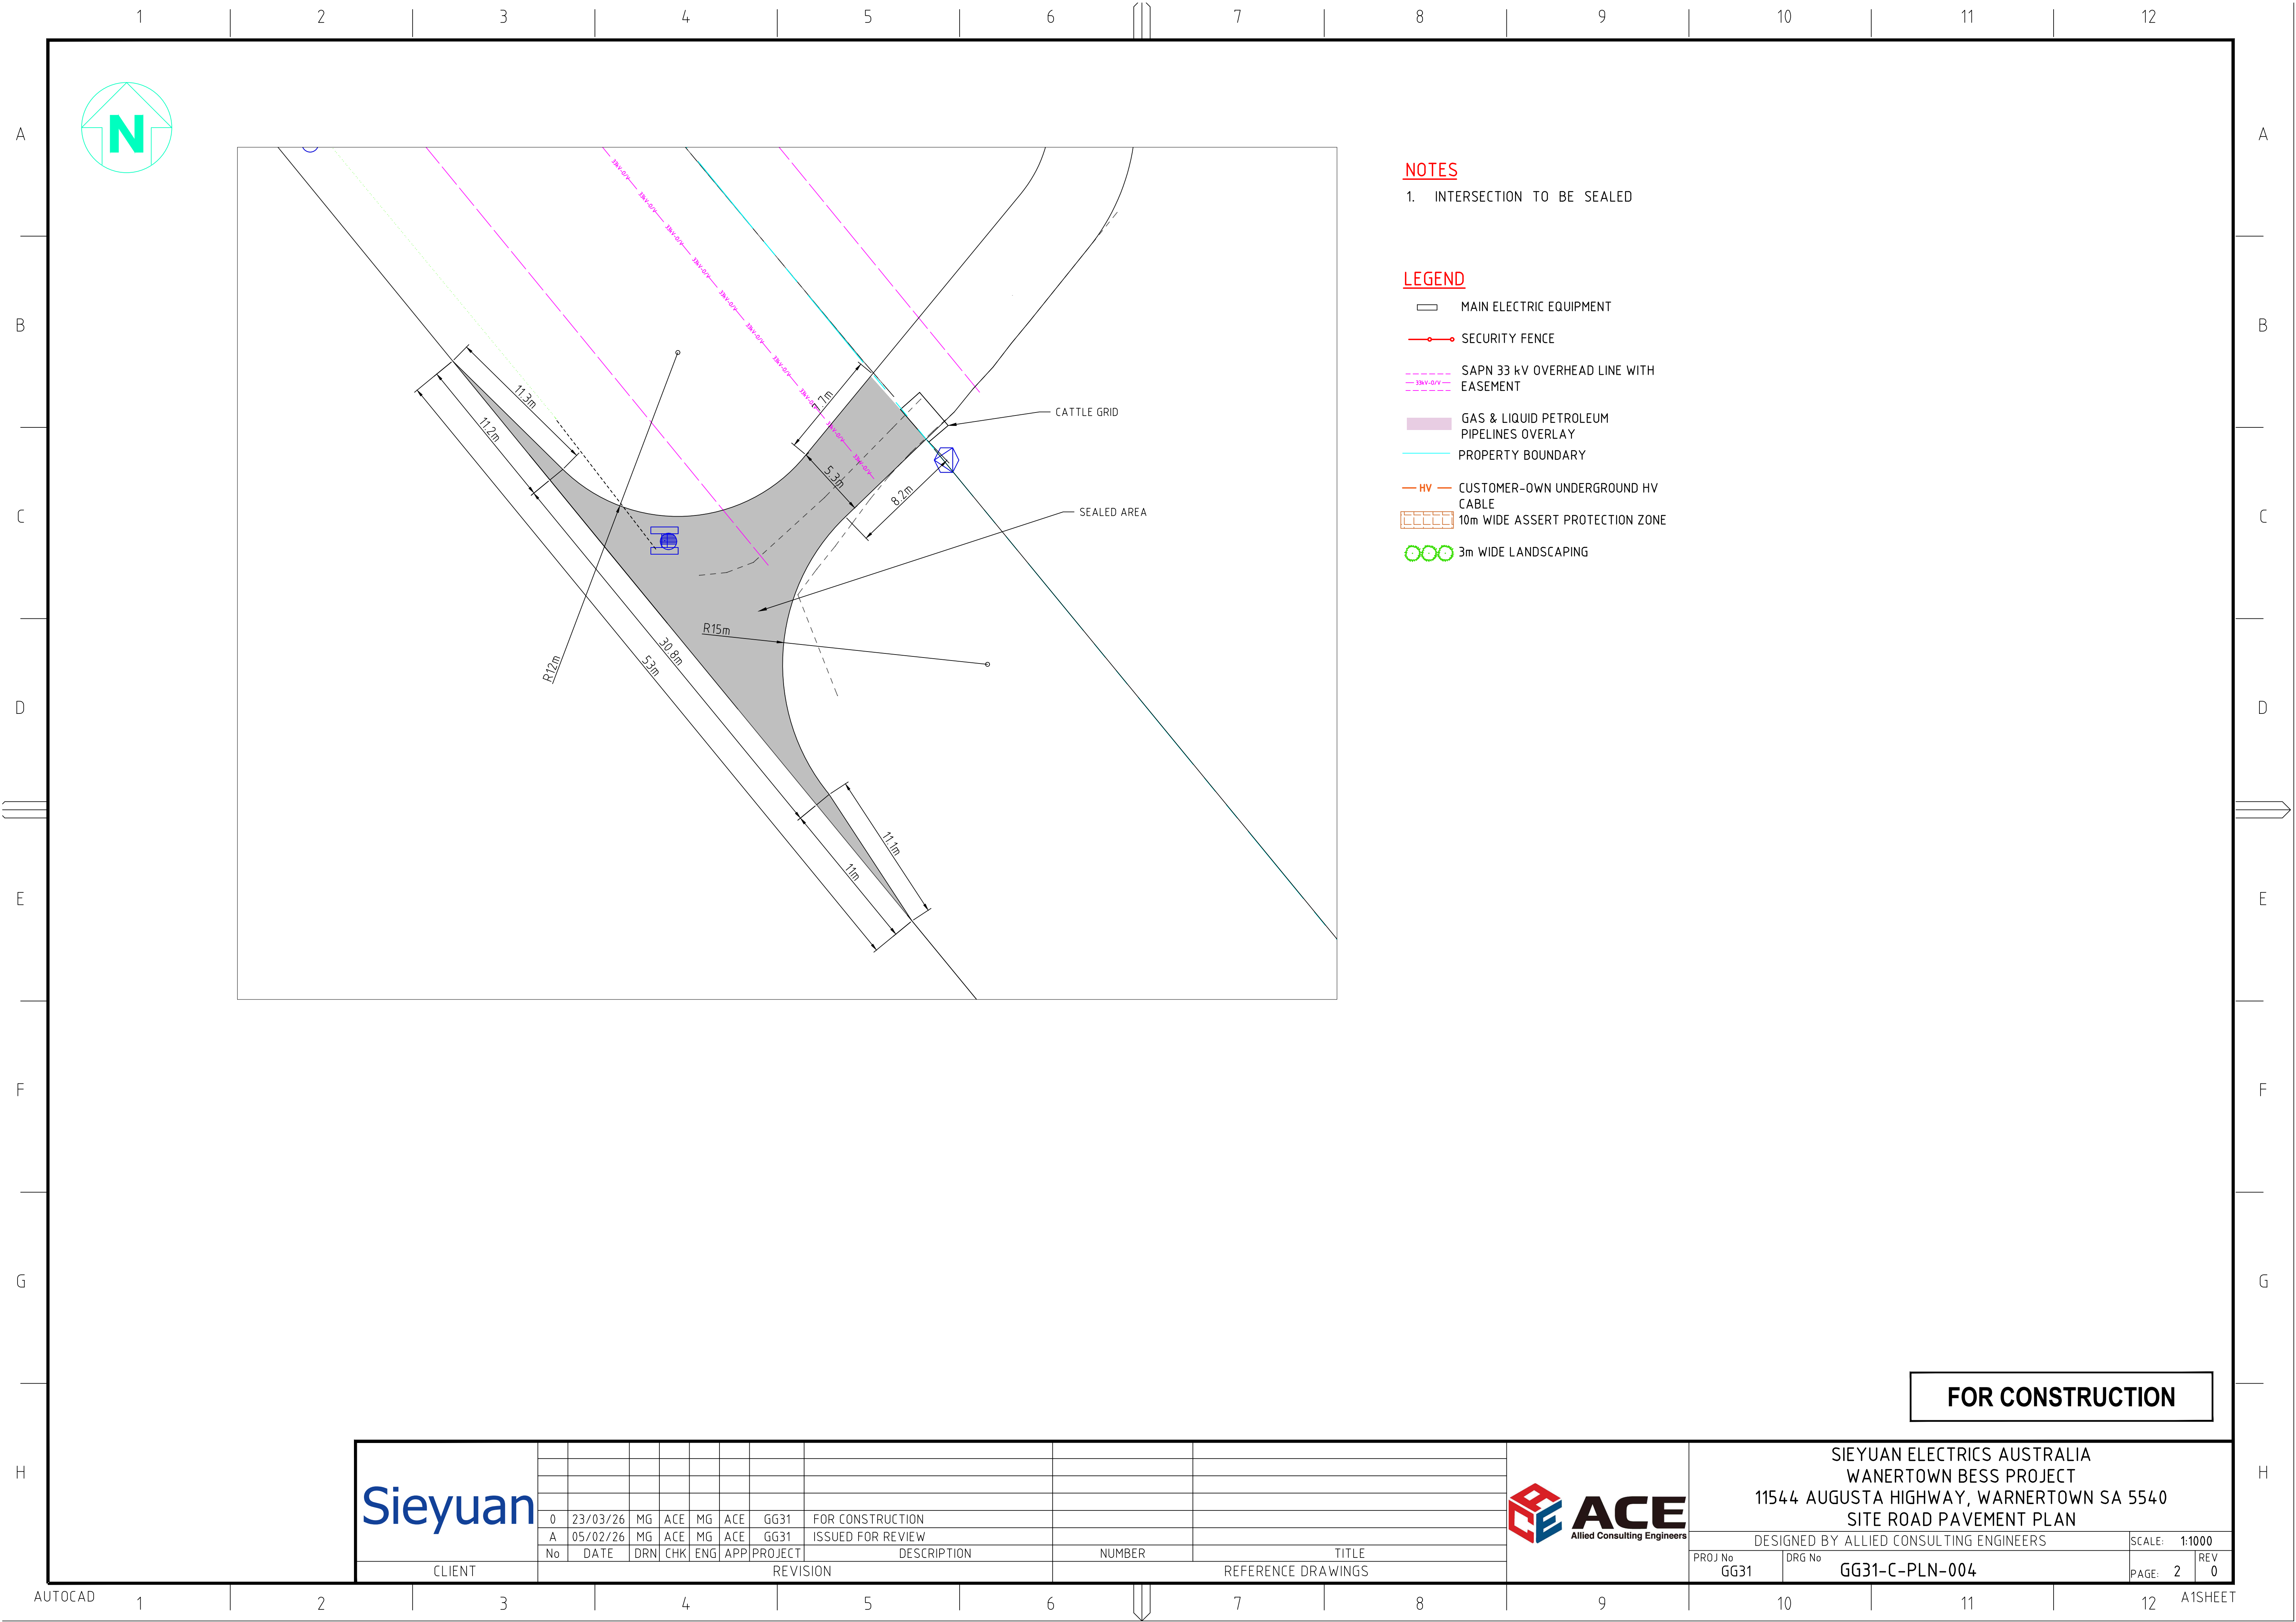

NOTES
1. INTERSECTION TO BE SEALED

- LEGEND**
- MAIN ELECTRIC EQUIPMENT
 - SECURITY FENCE
 - SAPN 33 kV OVERHEAD LINE WITH EASEMENT
 - GAS & LIQUID PETROLEUM PIPELINES OVERLAY
 - PROPERTY BOUNDARY
 - HV CUSTOMER-OWN UNDERGROUND HV CABLE
 - 10m WIDE ASSET PROTECTION ZONE
 - 3m WIDE LANDSCAPING

FOR CONSTRUCTION

Sieyuan												 ACE Allied Consulting Engineers	SIEYUAN ELECTRICS AUSTRALIA WANERTOWN BESS PROJECT 11544 AUGUSTA HIGHWAY, WARNERTOWN SA 5540 SITE ROAD PAVEMENT PLAN				
	0	23/03/26	MG	ACE	MG	ACE	GG31	FOR CONSTRUCTION					DESIGNED BY ALLIED CONSULTING ENGINEERS				
	A	05/02/26	MG	ACE	MG	ACE	GG31	ISSUED FOR REVIEW					SCALE: 1:1000				
	No	DATE	DRN	CHK	ENG	APP	PROJECT	DESCRIPTION	NUMBER	TITLE	PROJ No GG31		DRG No GG31-C-PLN-004	PAGE: 2	REV 0		
CLIENT	REVISION							REFERENCE DRAWINGS									