


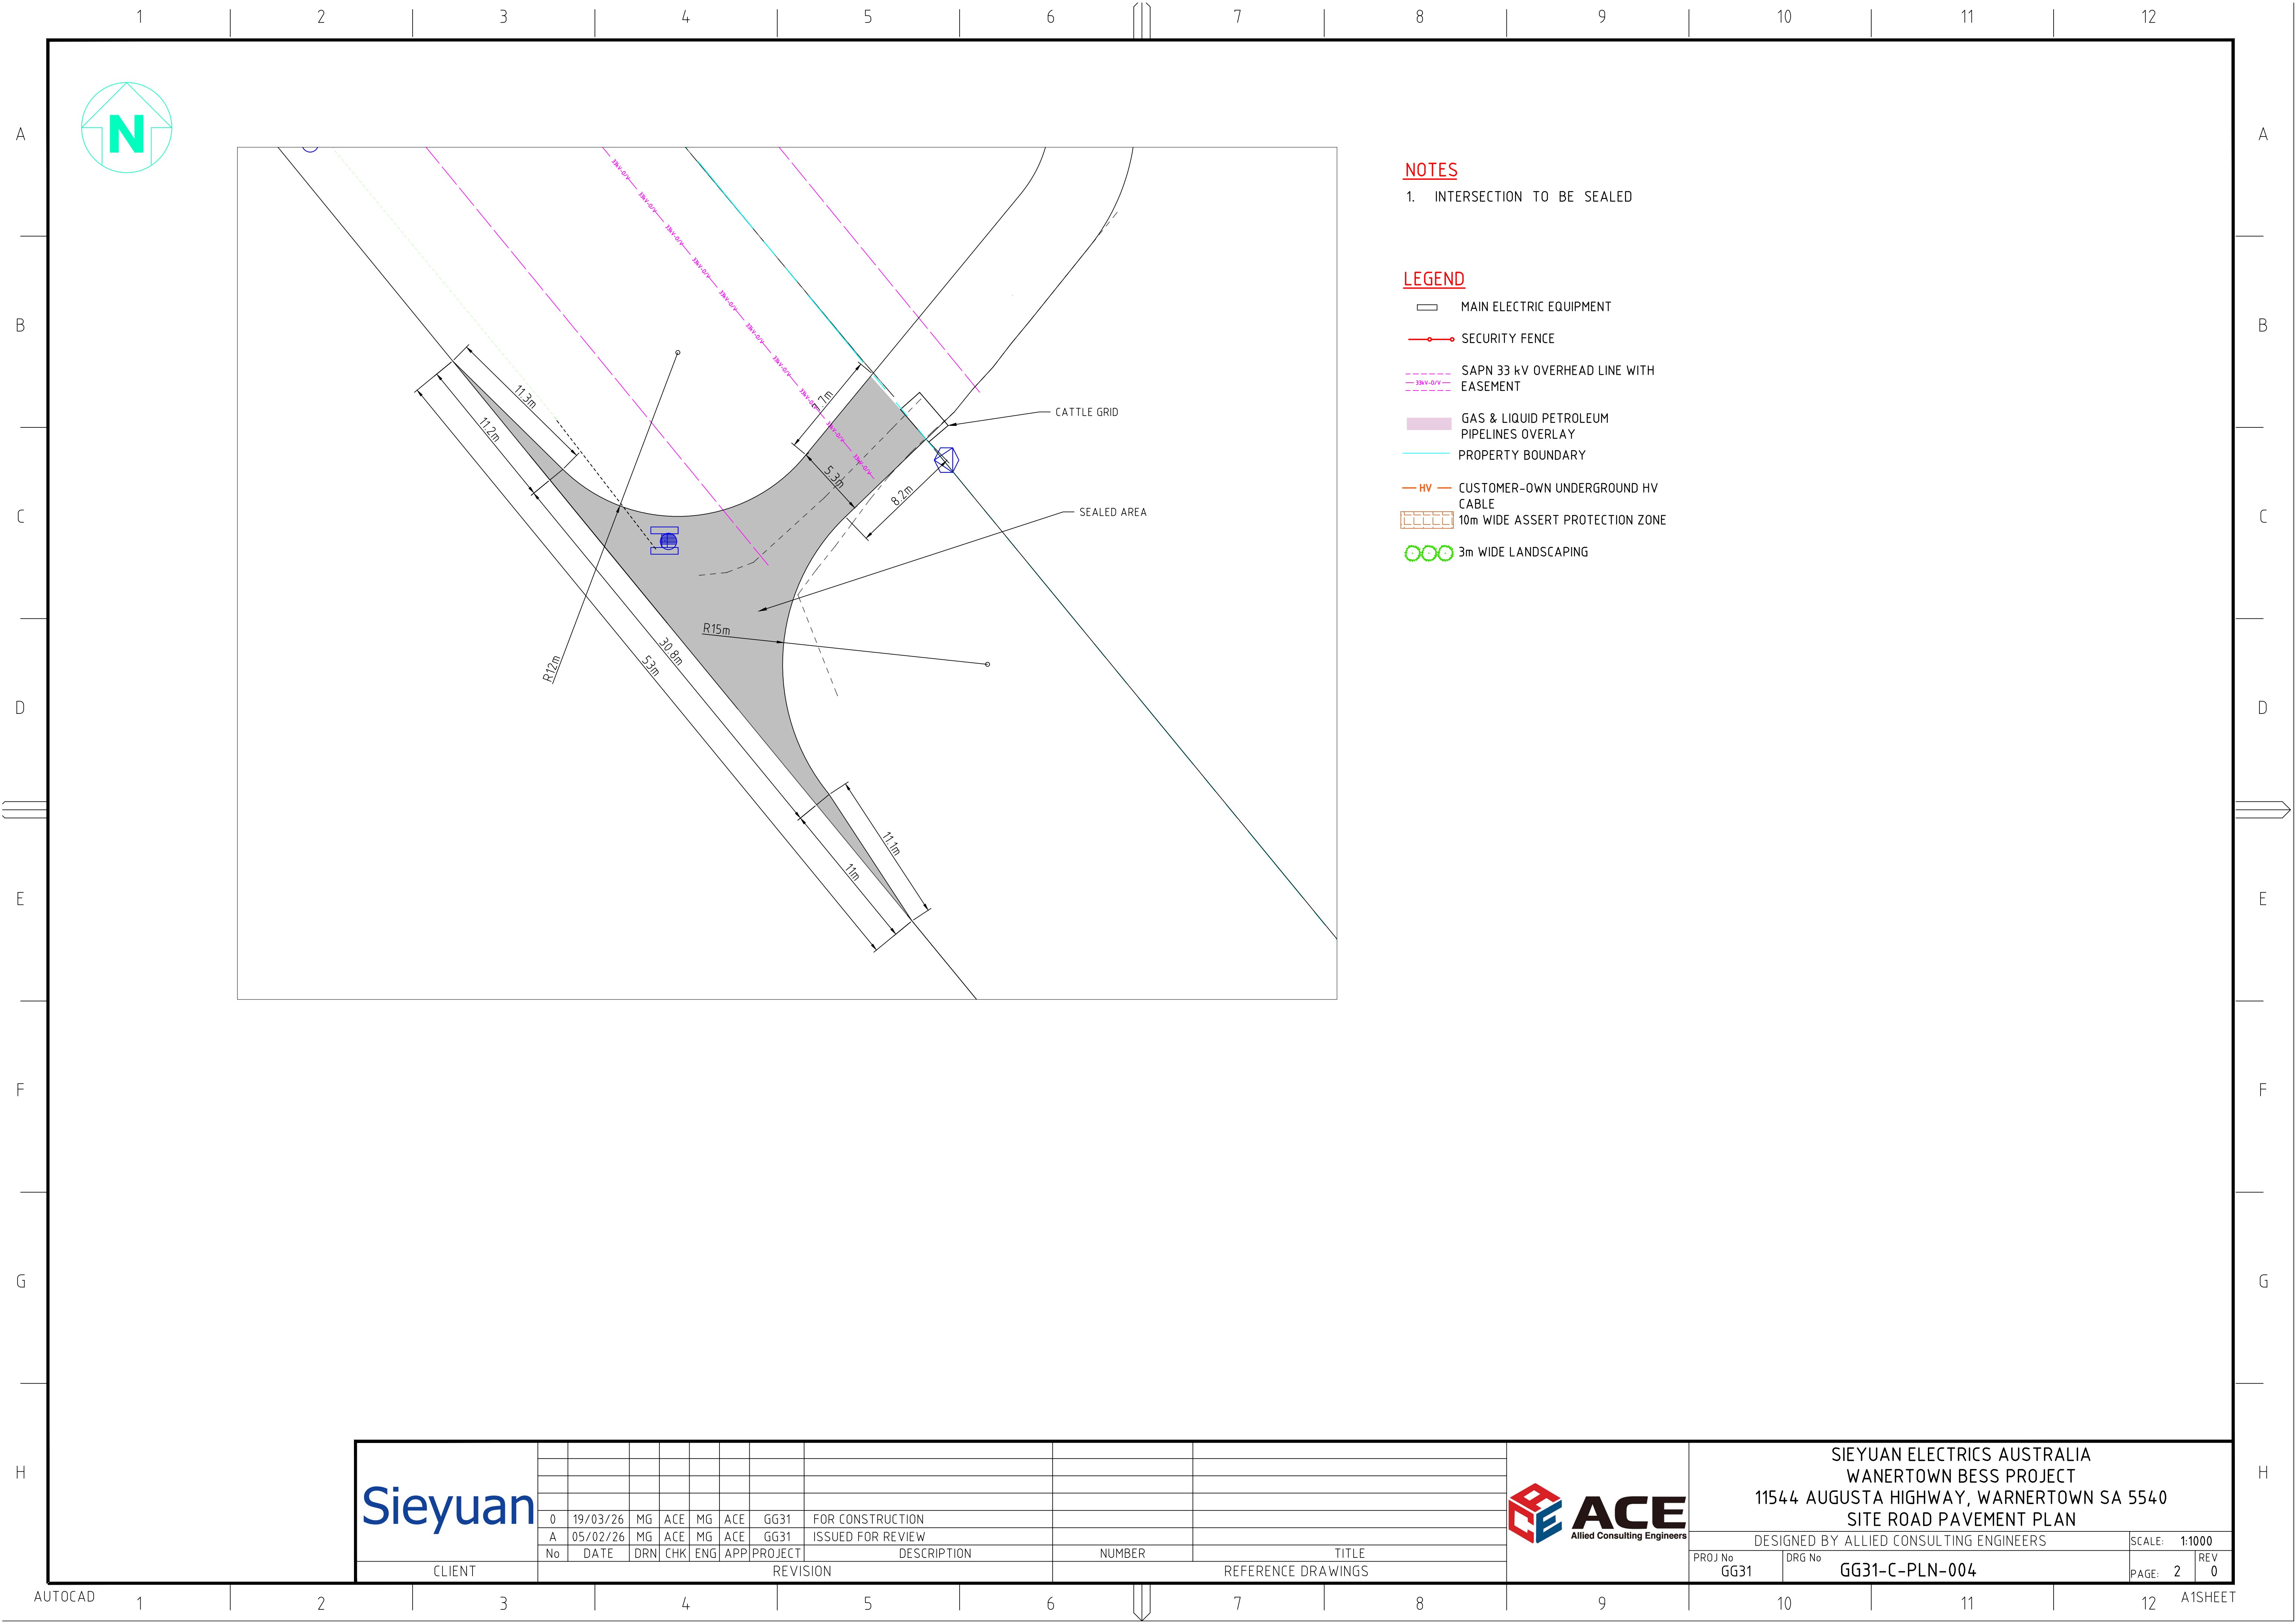

NOTES

1. INTERSECTION TO BE SEALED

LEGEND

- MAIN ELECTRIC EQUIPMENT
- SECURITY FENCE
- SAPN 33 kV OVERHEAD LINE WITH EASEMENT
- GAS & LIQUID PETROLEUM PIPELINES OVERLAY
- PROPERTY BOUNDARY
- HV CUSTOMER-OWN UNDERGROUND HV CABLE
- 10m WIDE ASSERT PROTECTION ZONE
- 3m WIDE LANDSCAPING

Sieyuan												SIEYUAN ELECTRICS AUSTRALIA WANERTOWN BESS PROJECT 11544 AUGUSTA HIGHWAY, WARNERTOWN SA 5540 SITE ROAD PAVEMENT PLAN			
	0	19/03/26	MG	ACE	MG	ACE	GG31	FOR CONSTRUCTION				DESIGNED BY ALLIED CONSULTING ENGINEERS			
	A	05/02/26	MG	ACE	MG	ACE	GG31	ISSUED FOR REVIEW				SCALE: 1:1000			
	No	DATE	DRN	CHK	ENG	APP	PROJECT	DESCRIPTION	NUMBER	TITLE		PROJ No	DRG No	PAGE	REV
CLIENT							REVISION			REFERENCE DRAWINGS		GG31	GG31-C-PLN-004	2	0